




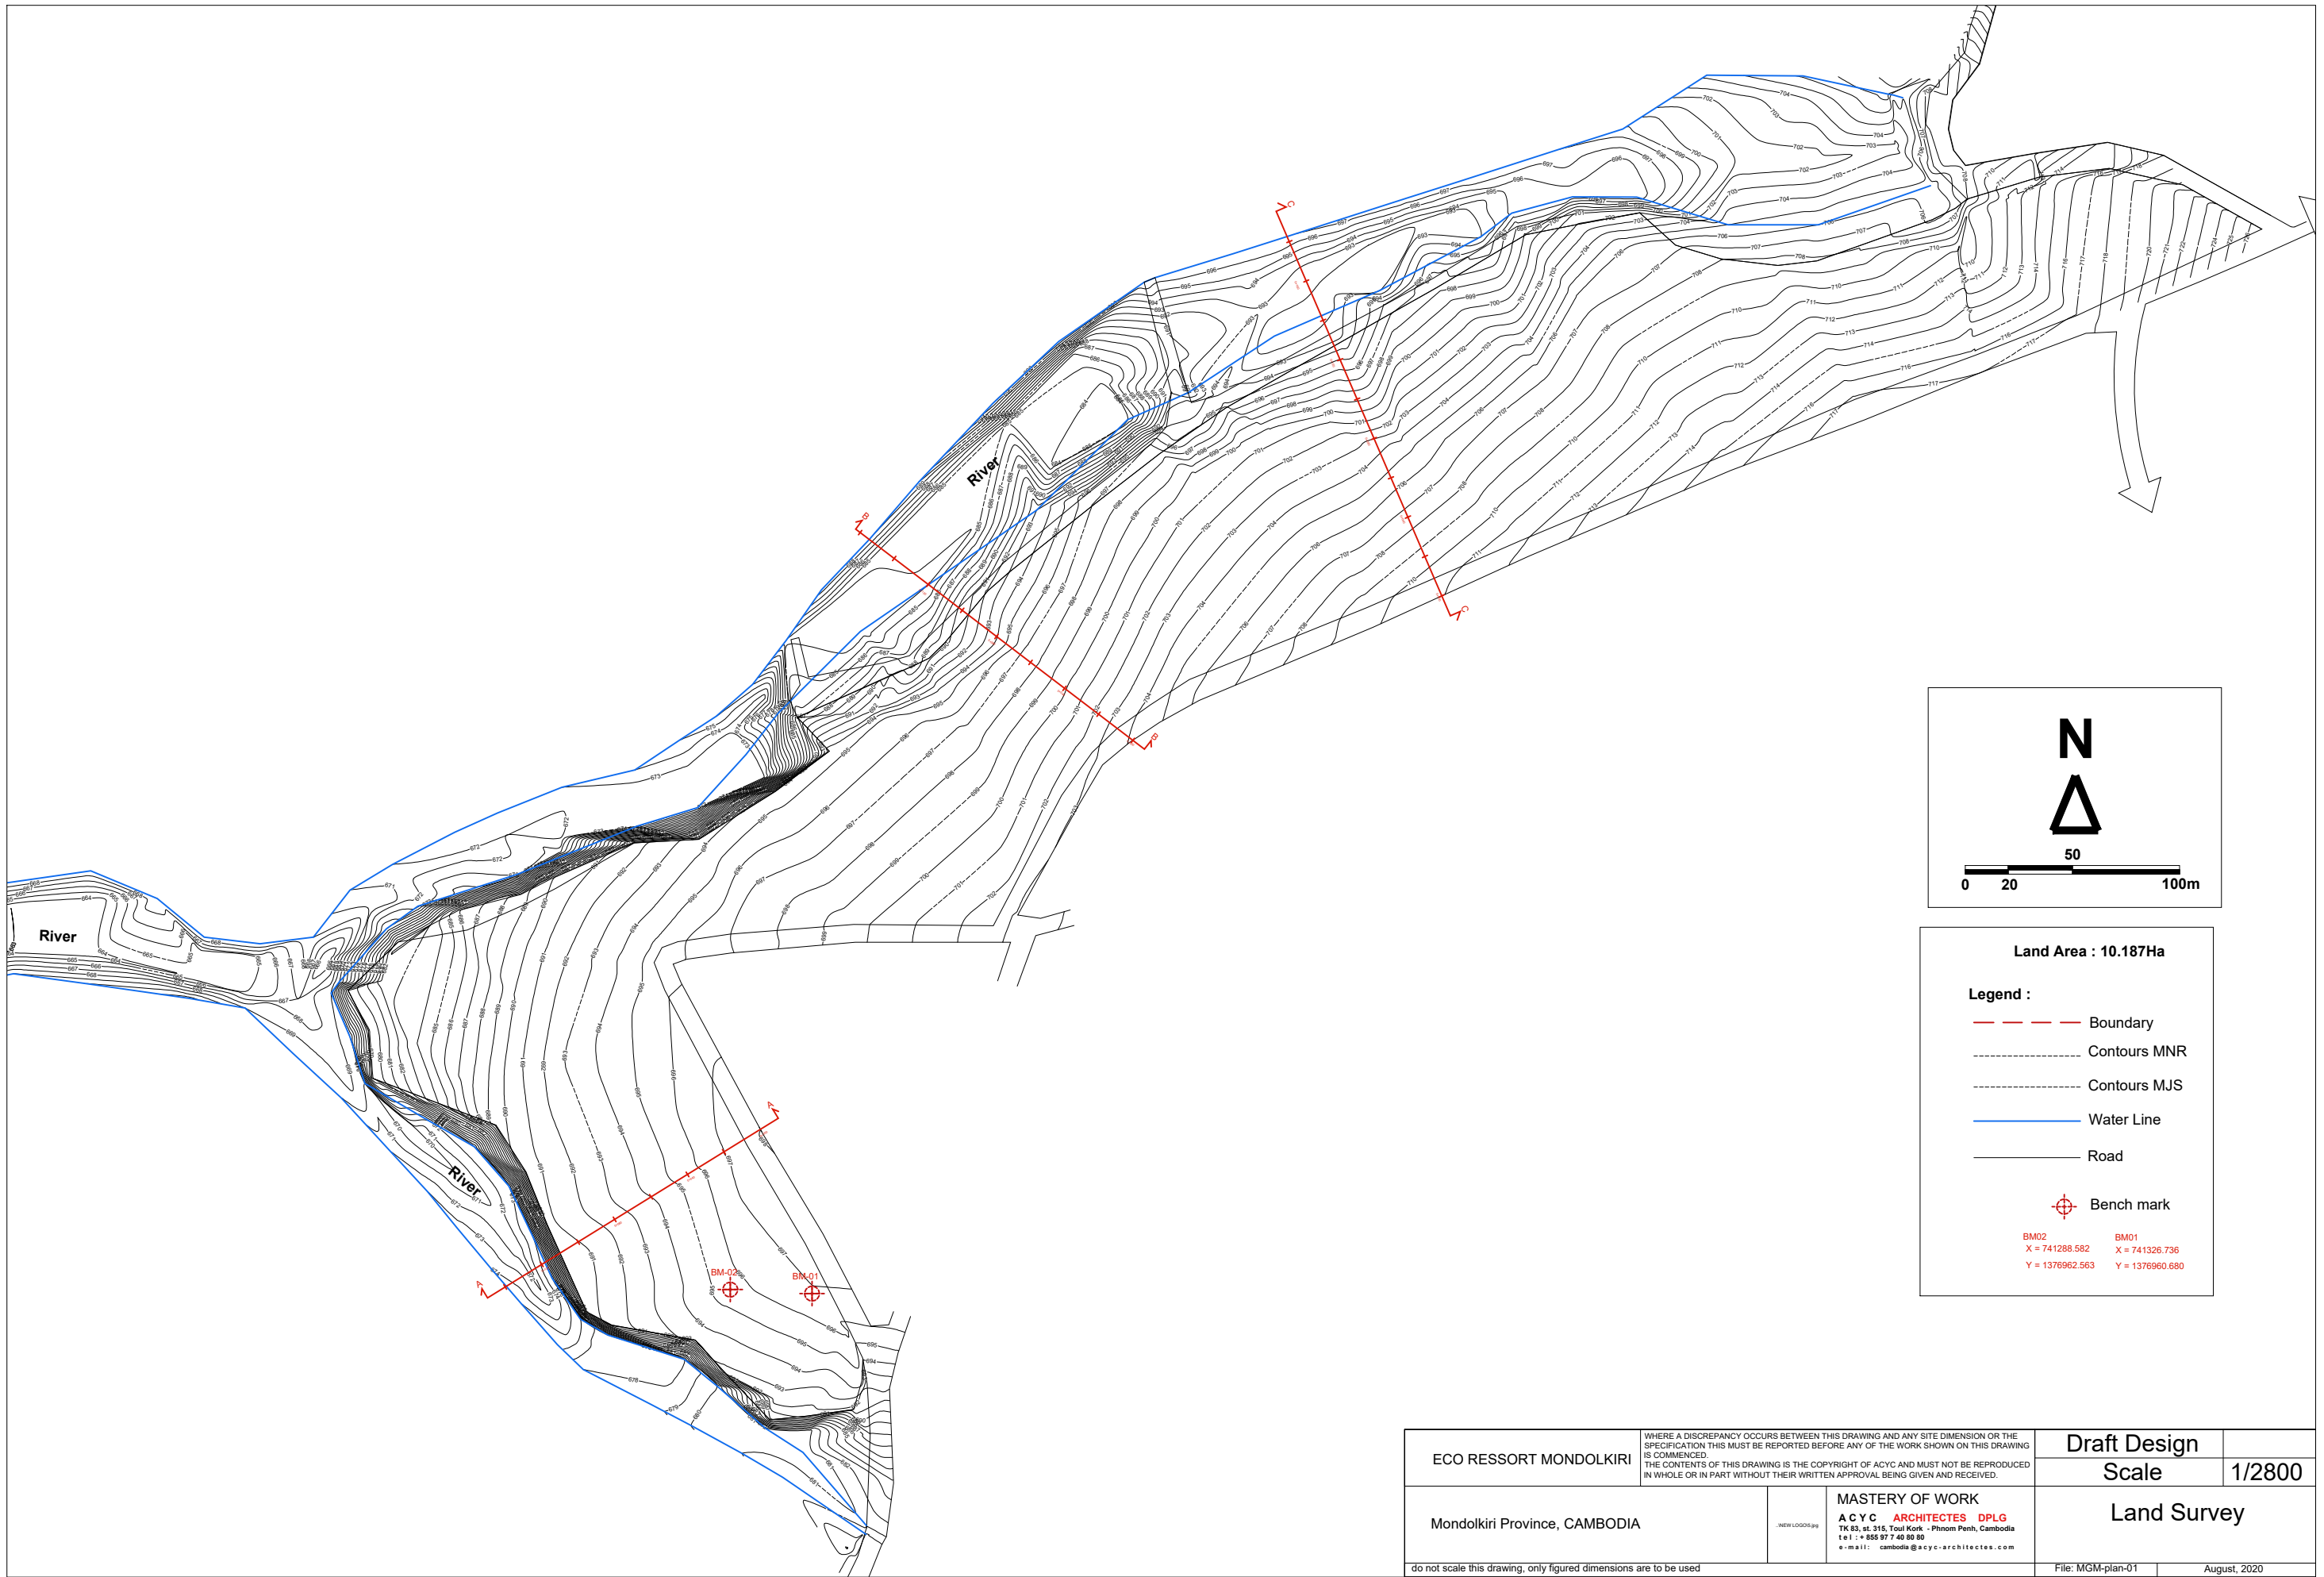


ECO RESSORT MONDOLKIRI		WHERE A DISCREPANCY OCCURS BETWEEN THIS DRAWING AND ANY SITE DIMENSION OR THE SPECIFICATION THIS MUST BE REPORTED BEFORE ANY OF THE WORK SHOWN ON THIS DRAWING IS COMMENCED. THE CONTENTS OF THIS DRAWING IS THE COPYRIGHT OF ACYC AND MUST NOT BE REPRODUCED IN WHOLE OR IN PART WITHOUT THEIR WRITTEN APPROVAL BEING GIVEN AND RECEIVED.		Draft Design	
Mondoliri Province, CAMBODIA		MASTERY OF WORK ACYC ARCHITECTES DPLG TK 83, st. 315, Toul Kork - Phnom Penh, Cambodia tel : +855 97 7 40 80 80 e-mail: cambodia@acyc-architectes.com		Scale	1/2800
do not scale this drawing, only figured dimensions are to be used		Land Survey		File: MGM-plan-01	August, 2020

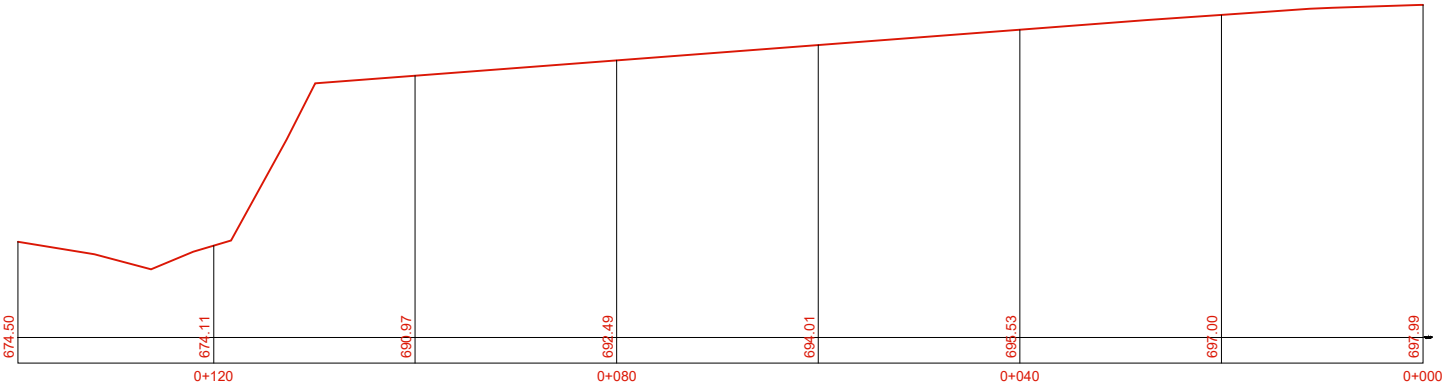

Section A-A

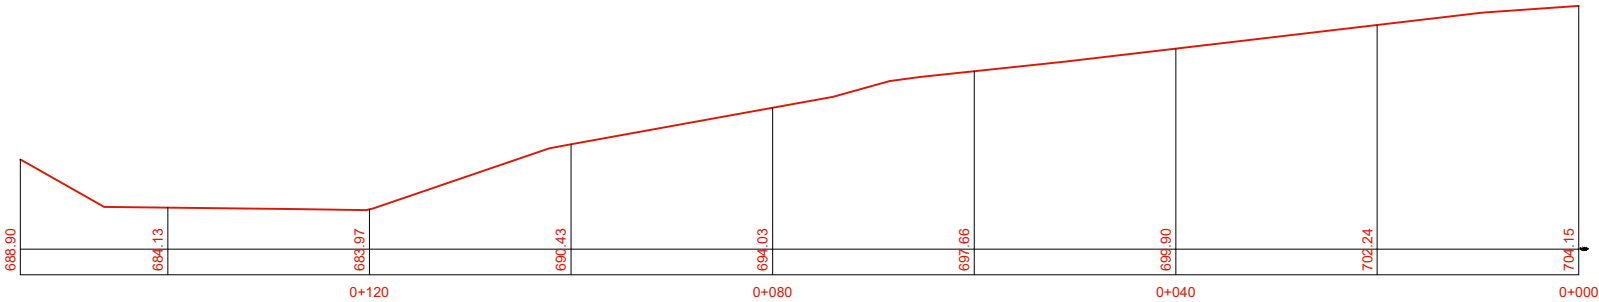

Section B-B

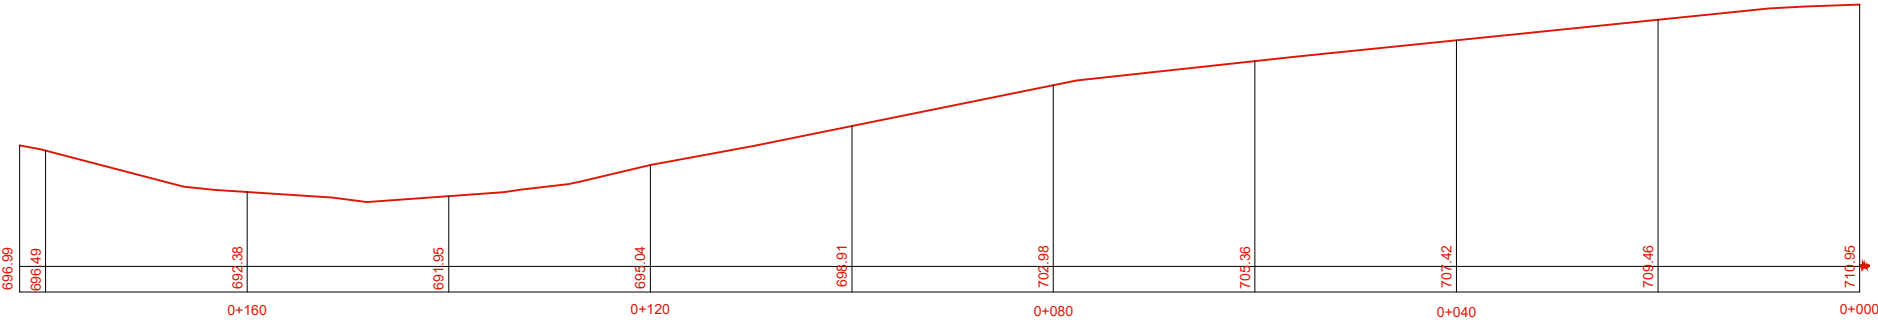

Section C-C

ECO RESSORT MONDOLKIRI		WHERE A DISCREPANCY OCCURS BETWEEN THIS DRAWING AND ANY SITE DIMENSION OR THE SPECIFICATION THIS MUST BE REPORTED BEFORE ANY OF THE WORK SHOWN ON THIS DRAWING IS COMMENCED. THE CONTENTS OF THIS DRAWING IS THE COPYRIGHT OF ACYC AND MUST NOT BE REPRODUCED IN WHOLE OR IN PART WITHOUT THEIR WRITTEN APPROVAL BEING GIVEN AND RECEIVED.		Draft Design	
Mondolkiri Province, CAMBODIA		MASTERY OF WORK ACYC ARCHITECTES DPLG TK 83, st. 315, Toul Kork - Phnom Penh, Cambodia tel : +855 97 7 40 80 80 e-mail: cambodia@acyc-architectes.com		Scale	1/750
do not scale this drawing, only figured dimensions are to be used				Land Survey Section Plan	
				File: MGM-plan-01	August, 2020